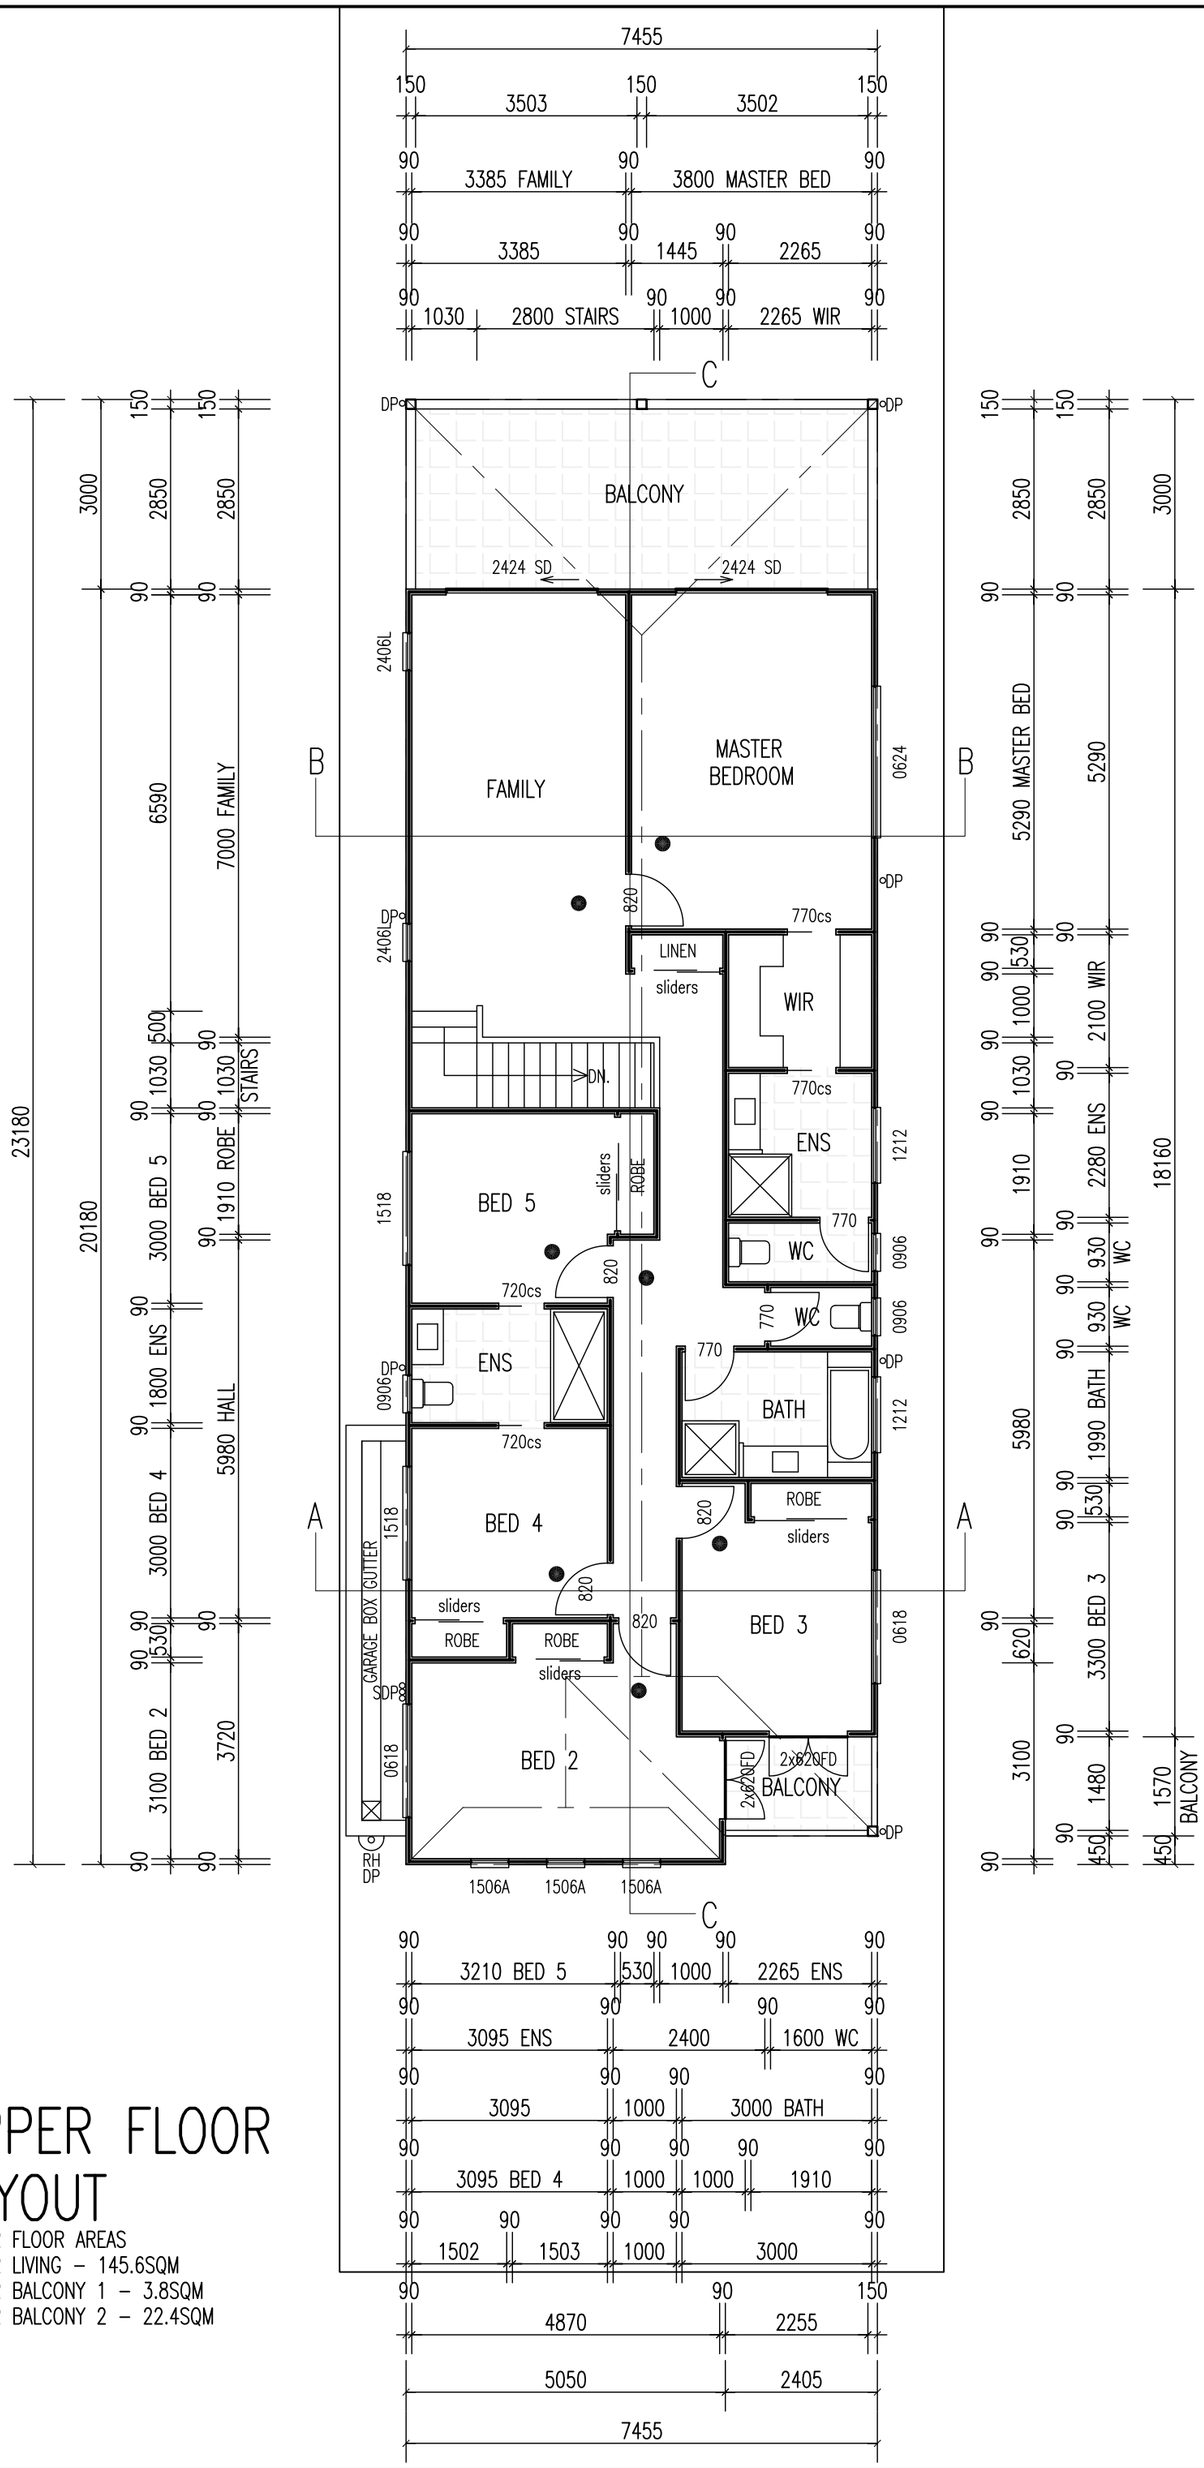


UPPER FLOOR LAYOUT

UPPER FLOOR AREAS
UPPER LIVING – 145.6SQM
UPPER BALCONY 1 – 3.8SQM
UPPER BALCONY 2 – 22.4SQM

● – LOCATION OF SMOKE ALARMS

SMOKE ALARMS TO COMPLY WITH THE NCC 2022 VOL 2 PART 9.5 AND THE BUILDING REGULATIONS AS3786–2014. SMOKE ALARMS MUST BE PHOTOELECTRIC, HARD WIRED AND INTERCONNECTED.

WATERPROOFING TO BE CARRIED OUT IN ACCORDANCE WITH THE BCA VOL 2 PART 3.8.1 & INSTALLED BY A QUALIFIED PERSON

WC DOORS TO COMPLY WITH THE BCA, PART 3.8.3. DOOR TO SWING OUT FROM EDGE OF THE PAN, DISTANCE BETWEEN THE PAN & & THE DOOR TO BE MIN 1200MM OR LIFT–OFF HINGES TO BE INSTALLED.

NERANG CREATIVE design
NCD BUILDING DESIGNERS
www.nerangcreative.com.au

PH: (07)55 781622
FAX: (07)55 961294
EMAIL: ncd@nerangcreative.com.au
ADDRESS:
Suite 26, Advance Business Centre,
39-47 Lawrence Drive, Nerang.
POSTAL:
P.O. Box 587, Nerang, QLD, 4211.
QBCC License number: 1032939
ABN: 31 304 914 965

PROJECT:
NEW RESIDENCE

CLIENT:
SARAH BUTLER

PROJECT LOCATION:
LOT 470 RP26062 No.38
REUBEN STREET,
STAFFORD

REVISION TABLE

Revision	Description	Date

DATE: 26.08.2024

SCALE: 1:100

DRAWN: JM

CHECKED:

TITLE:
UPPER FLOOR LAYOUT

SHEET SIZE:
A3

JOB NUMBER:
NCD090/24

SHEET NUMBER
of 15

PDF-XChange Editor Click to BUY NOW! www.tracker-software.com